



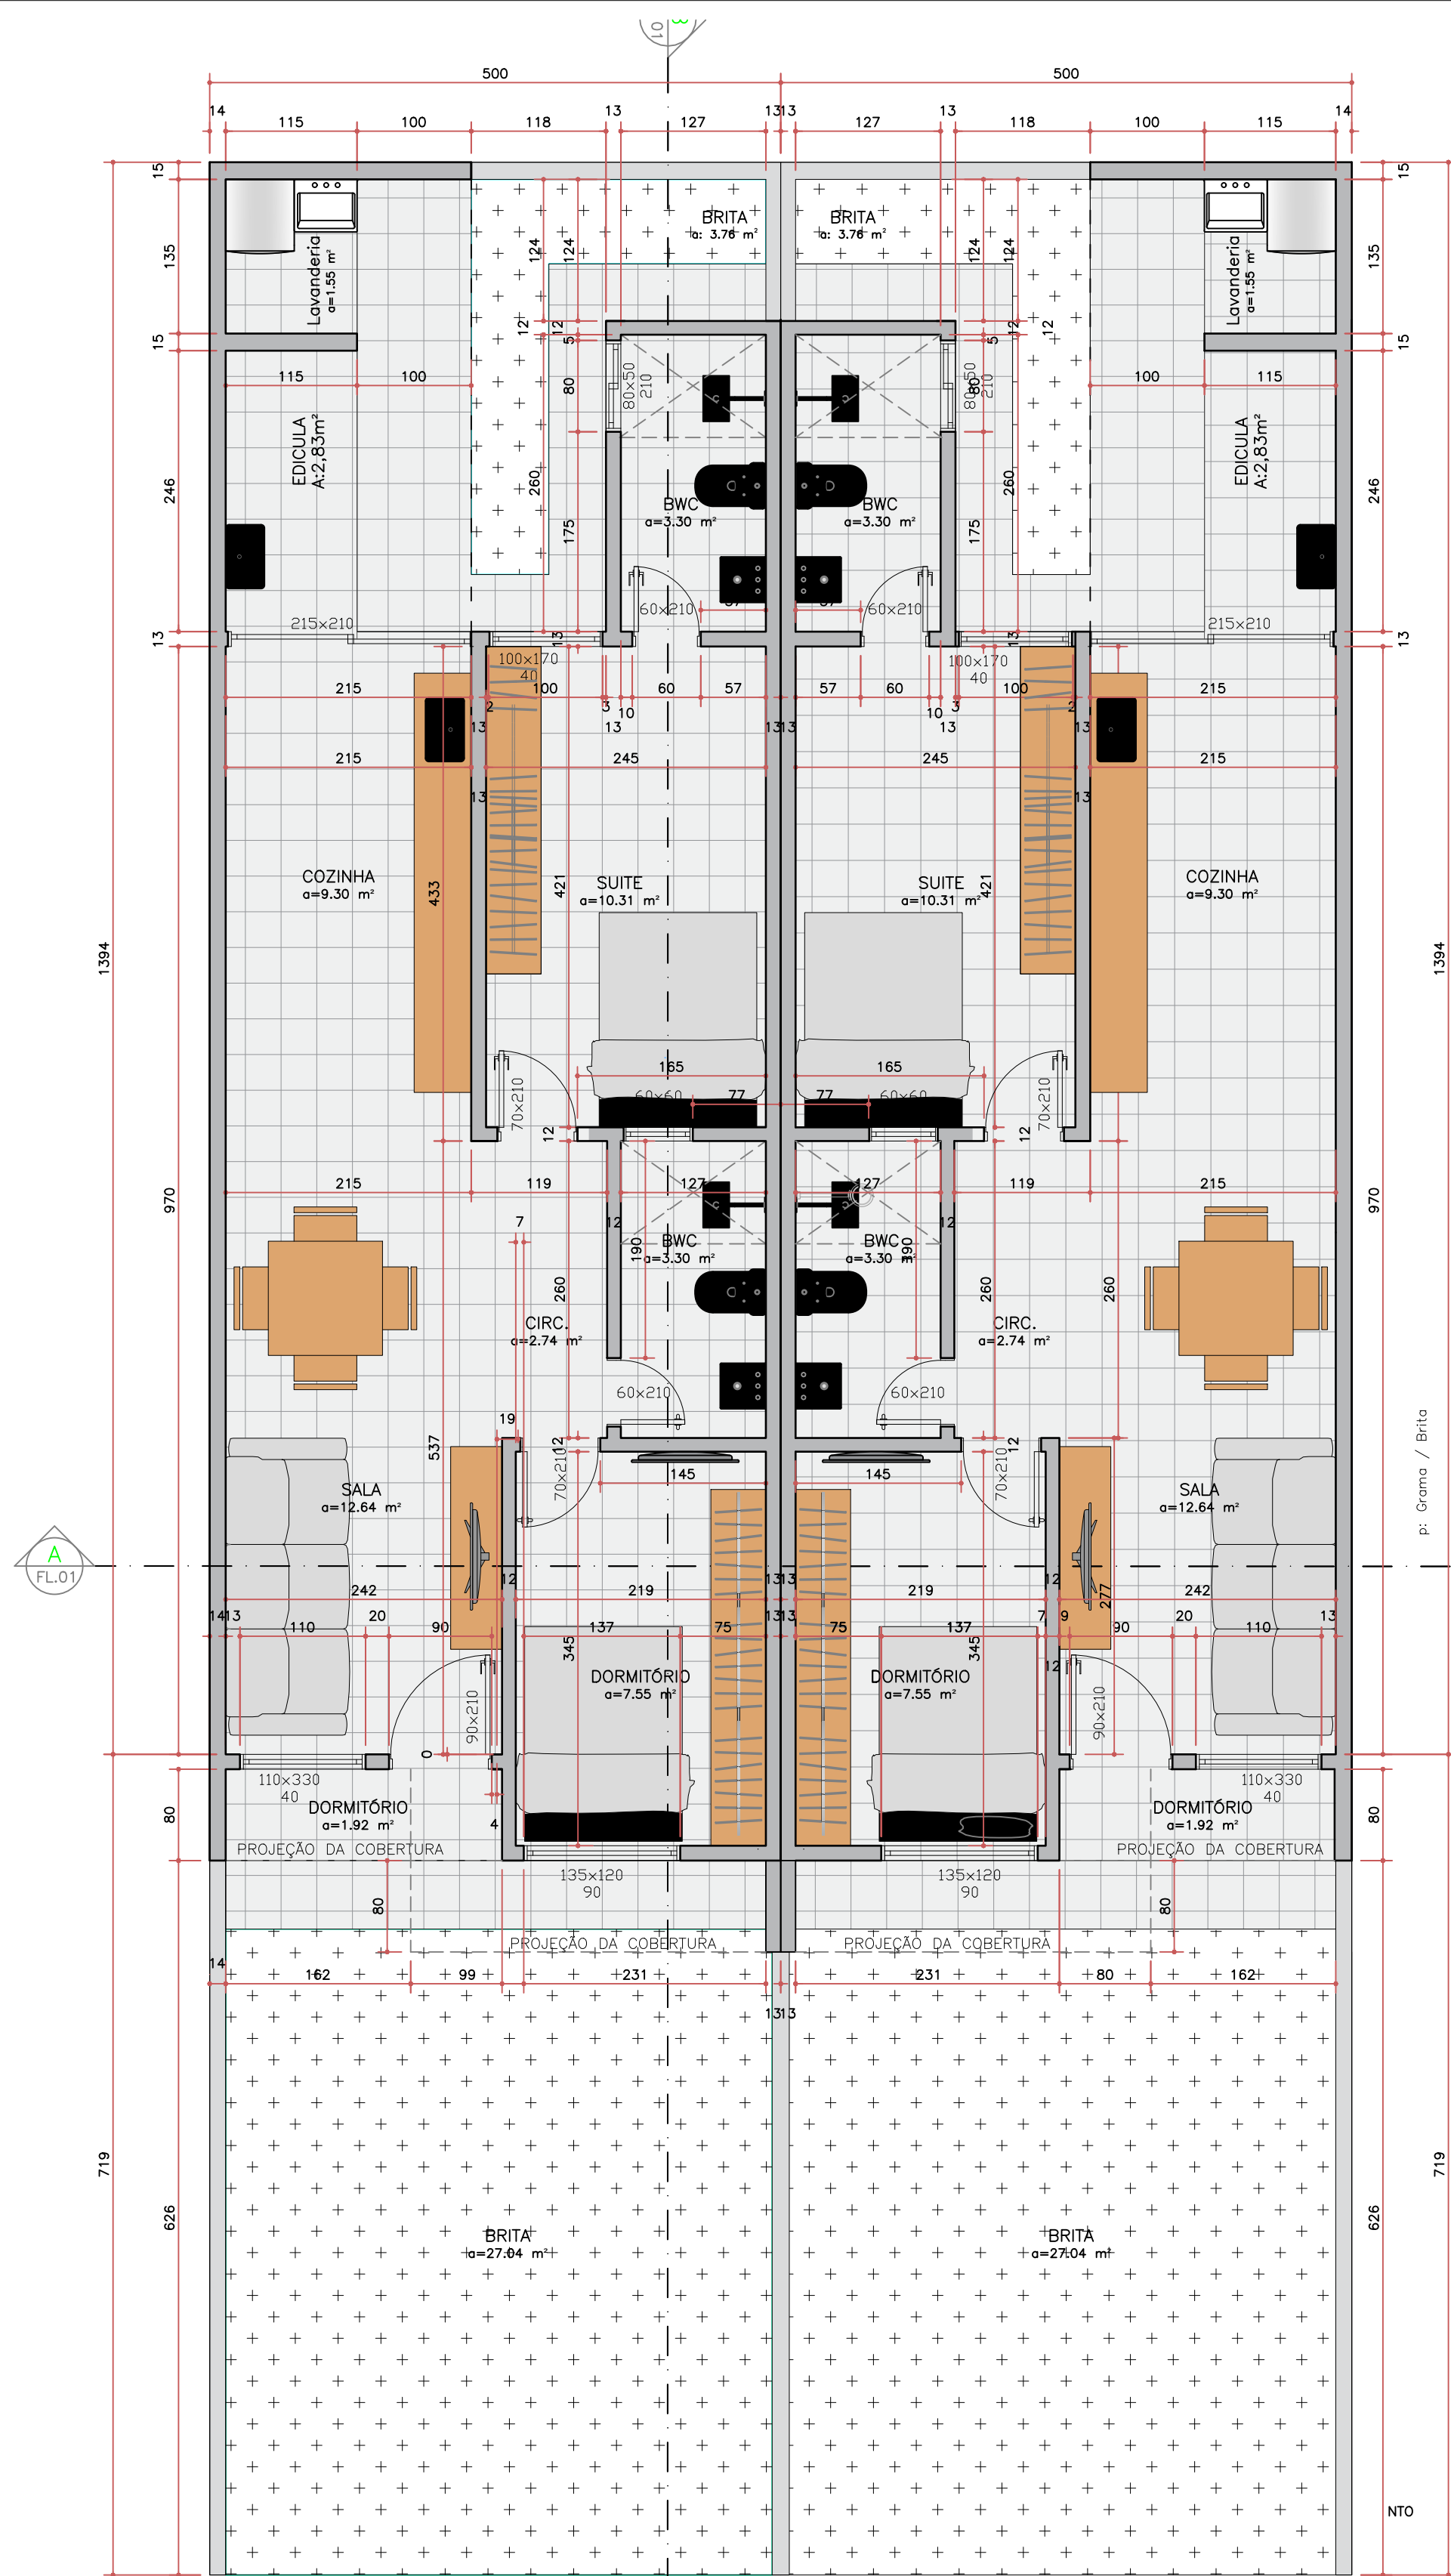

PLANTA BAIXA
ÁREA: 63,26m²

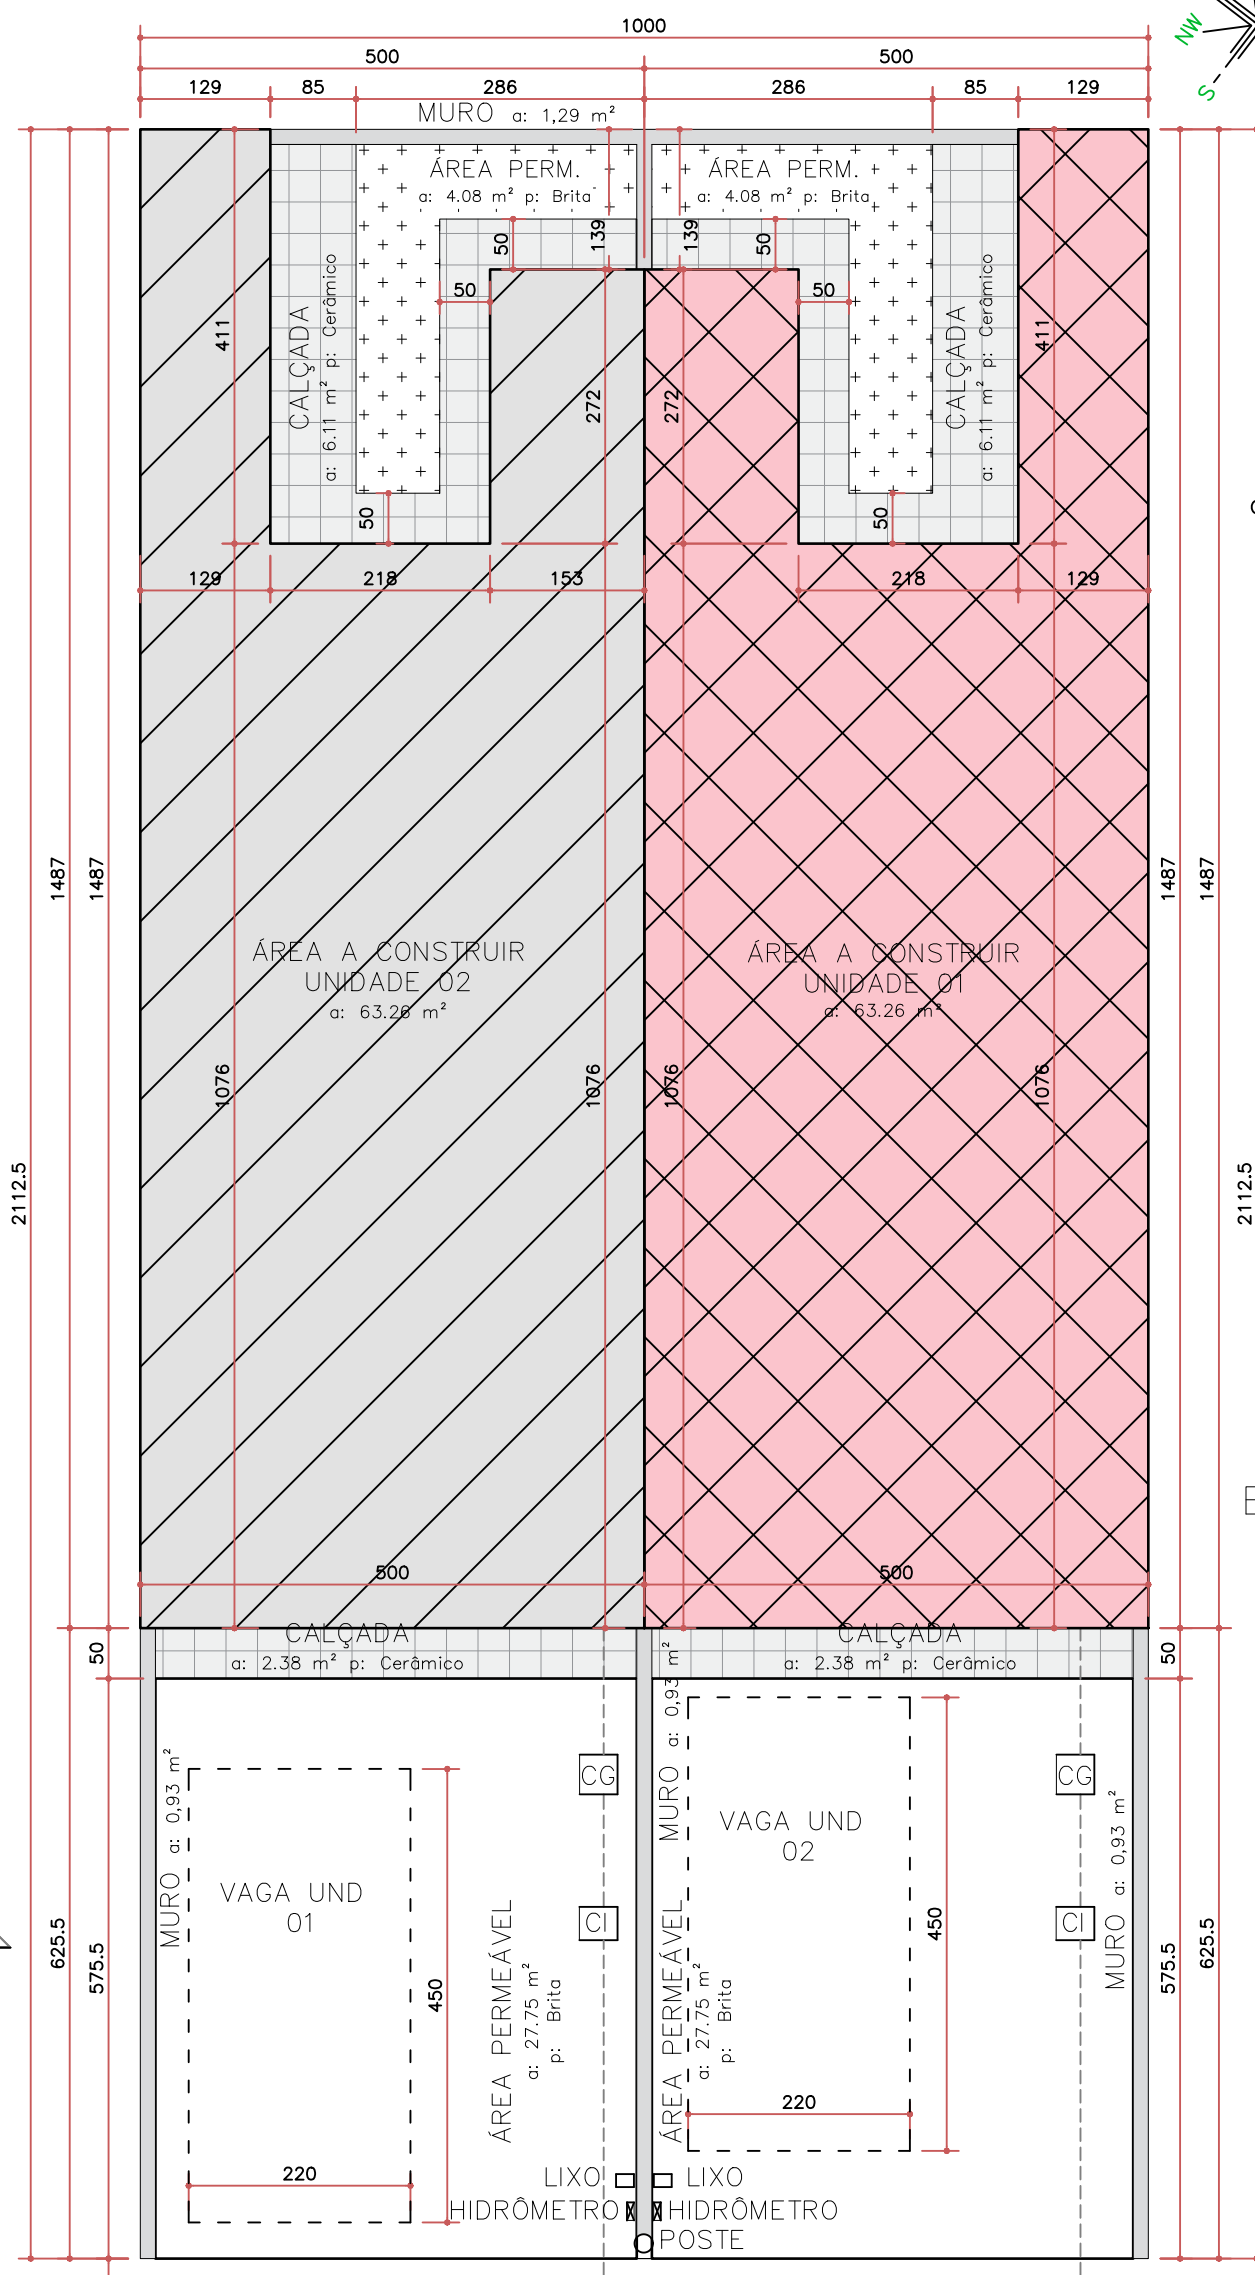

calçada de acordo com a lei nº 5.744/2011
piso antiderrapante 1:2%





25 200 450 200 125

GUIA REBAIXADA R. JOSÉ NUNES

SITUAÇÃO

ESCALA: 1/75

CORTE A1
ESCALA: 1/50

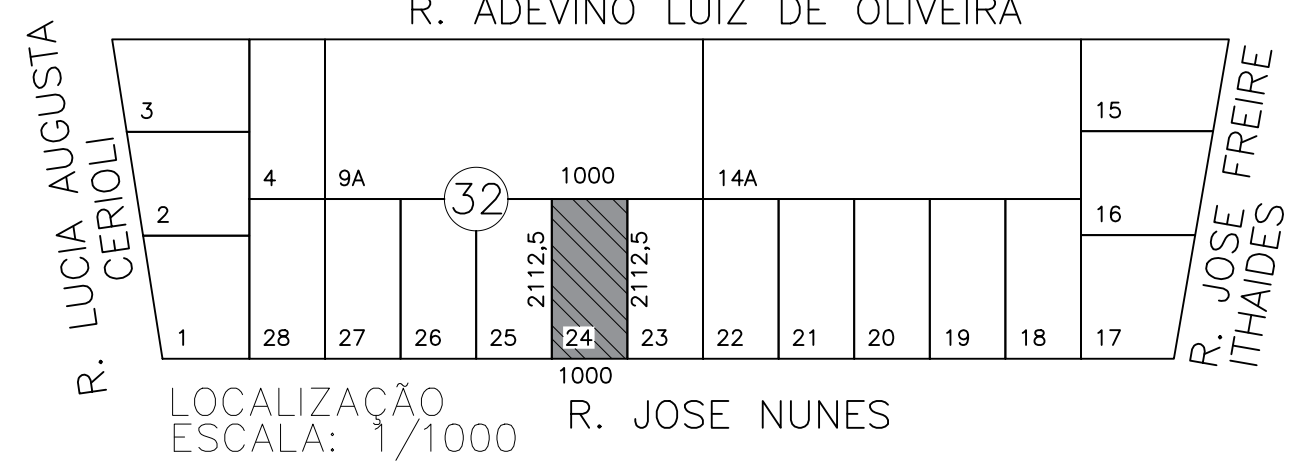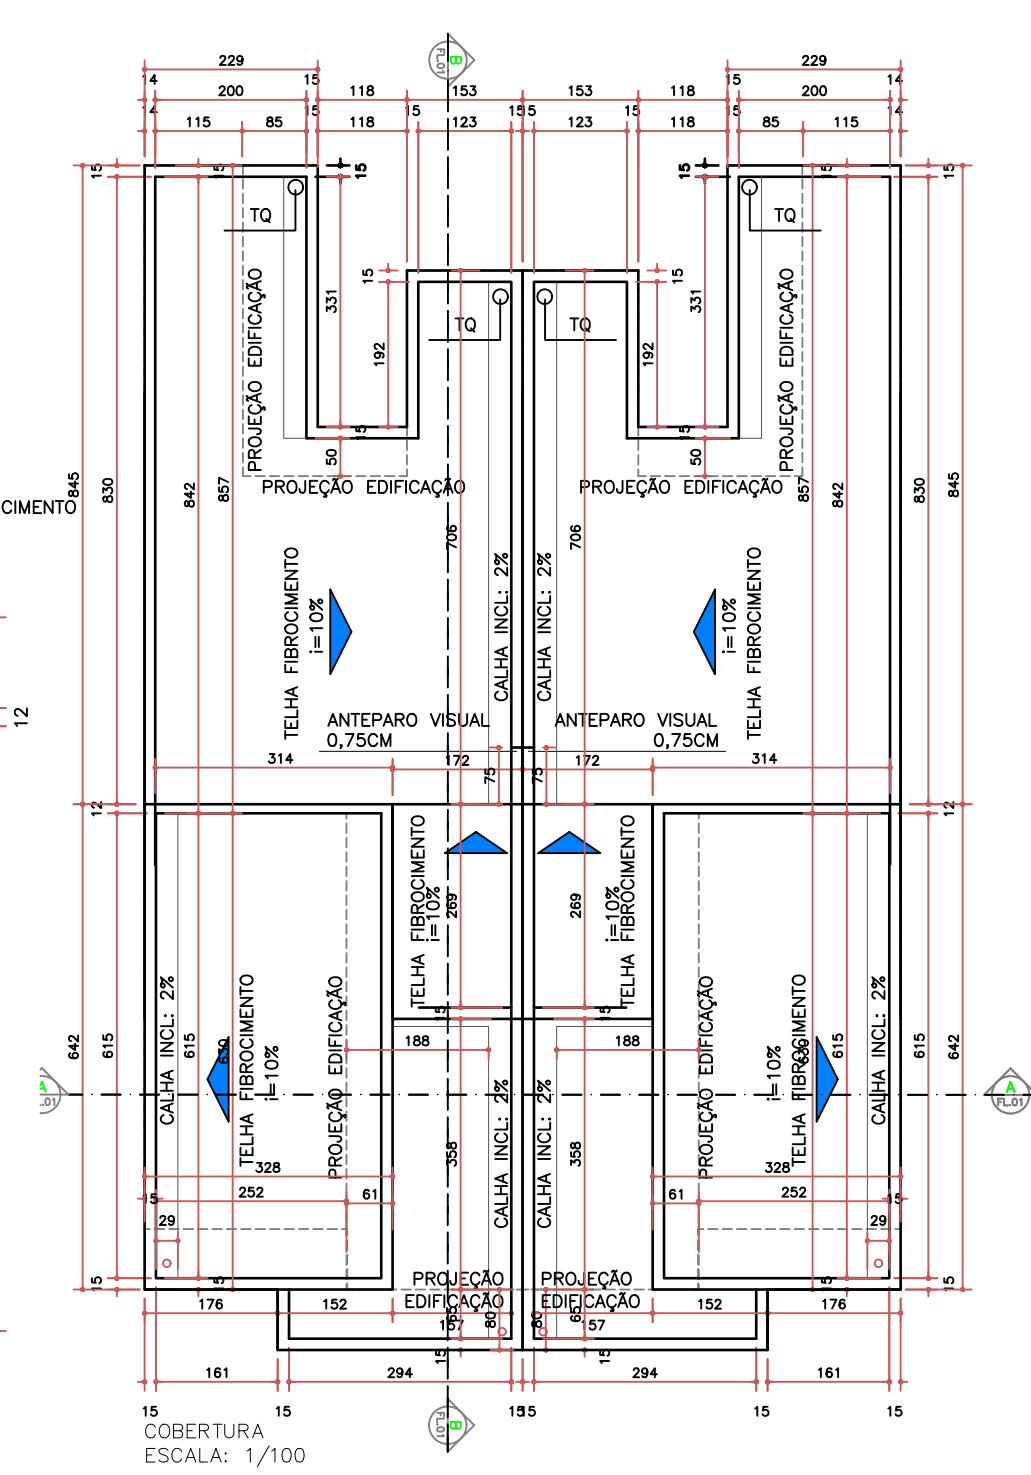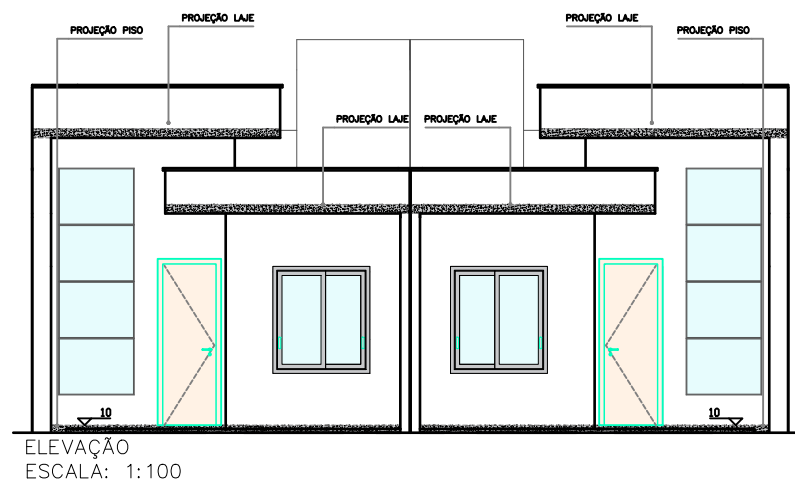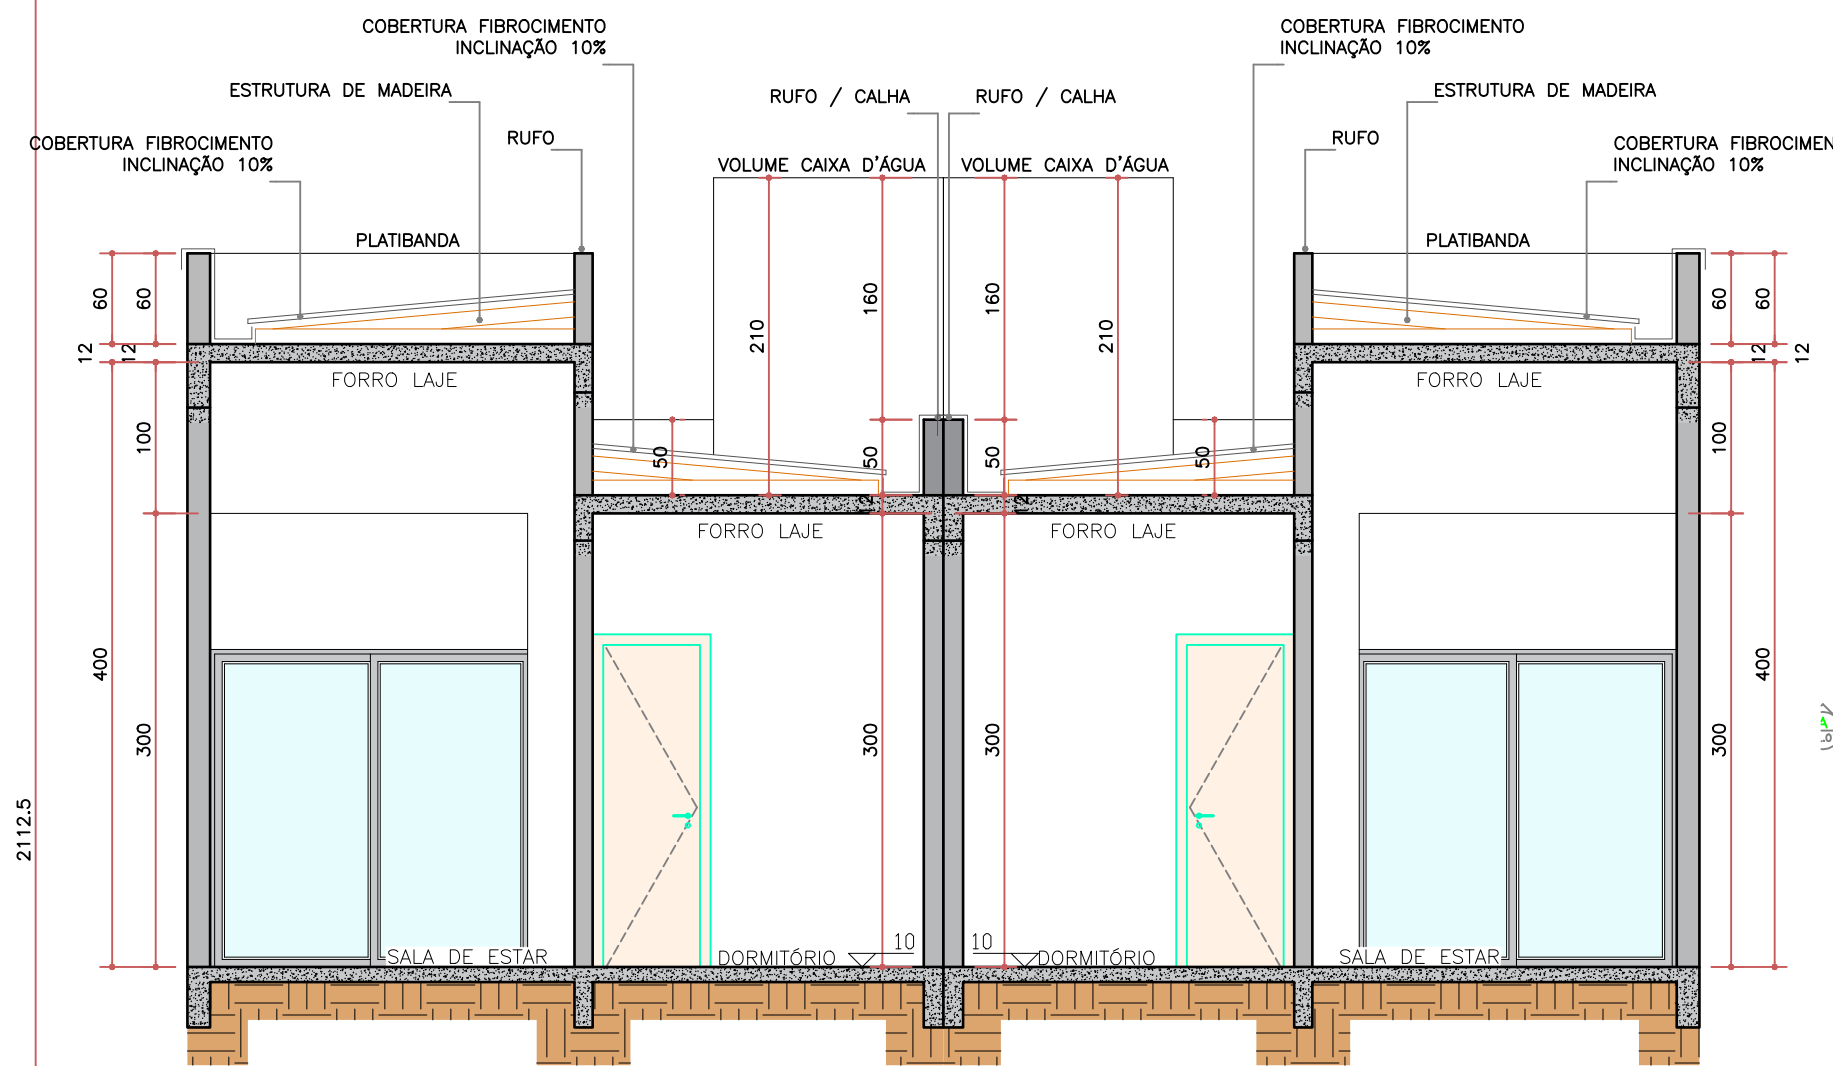

- NOTAS
- COTAS EM CENTÍMETROS;
 - COTAS DE NÍVEL EM METROS;
 - CONFERIR MEDIDAS, NÍVEIS E PRUMOS NO LOCAL;
 - MEDIDAS EM COTAS PREVALECEM SOBRE O DESENHO;
 - ESSE DESENHO DEVE SER IMPRESSO COLORIDO;

DATA	DESENHO	RESPONSÁVEL	FOLHA
16/06/2025	MAYCON ALMEIDA	MAYCON ALMEIDA	01
ESCALA	ARQUIVO	FASE	
ESCALA	2025.02.27_ANDRE E GODOY.DWG		
COD. DO PROJETO	DISCIPLINA	FASE	
0025	ARQUITETONICO EXECUTIVO		

LOCALIZAÇÃO	
ÁREA DO TERRENO	211,25 m ²
ÁREA A CONSTRUIR UNIDADE 01	63,26 m ²
ÁREA A CONSTRUIR UNIDADE 02	63,26 m ²
ÁREA TOTAL A CONSTRUIR	126,52 m ²
ÁREA DE CALÇADAS	16,98 m ²
ÁREA DE MURIS	4,12 m ²
ÁREA TOTAL IMPERMEABILIZADA	147,62 m ²
TAXA DE OCUPAÇÃO	29,88 %
COEFICIENTE DE APROPRIAMENTO	0,5989
TAXA DE PERMEABILIDADE	30,12 %

TÍTULO PLANTA BAIXA

TRABALHO DESENVOLVIDO POR:

Projeto Arquitetônico
Maycon Felipe de Almeida
CAU PR: 170768-4

Execução de Obra
Maycon Felipe de Almeida
CAU PR: 170768-4

PROPRIETÁRIO
Aureo Godoy
CPF: 053.548.509-32